
PLANTA TOPOGRÁFICA

ESCALA 1:550

SIMBOLOGÍA · PROPUESTA DE LOTES Y CAMINOS

- Camino principal 6 m (V1·V2·V3): 2 m en el predio + 4 m del vecino
- Camino interno privado 4 m: 147 m, retorno de 12 m de diámetro
- Línea eléctrica propuesta
- Punto a marcar por el topógrafo (ver tabla)
- Lote (7 lotes)
- Escuela Tribu: recinto 600 m² en la donación de 2,500 m²

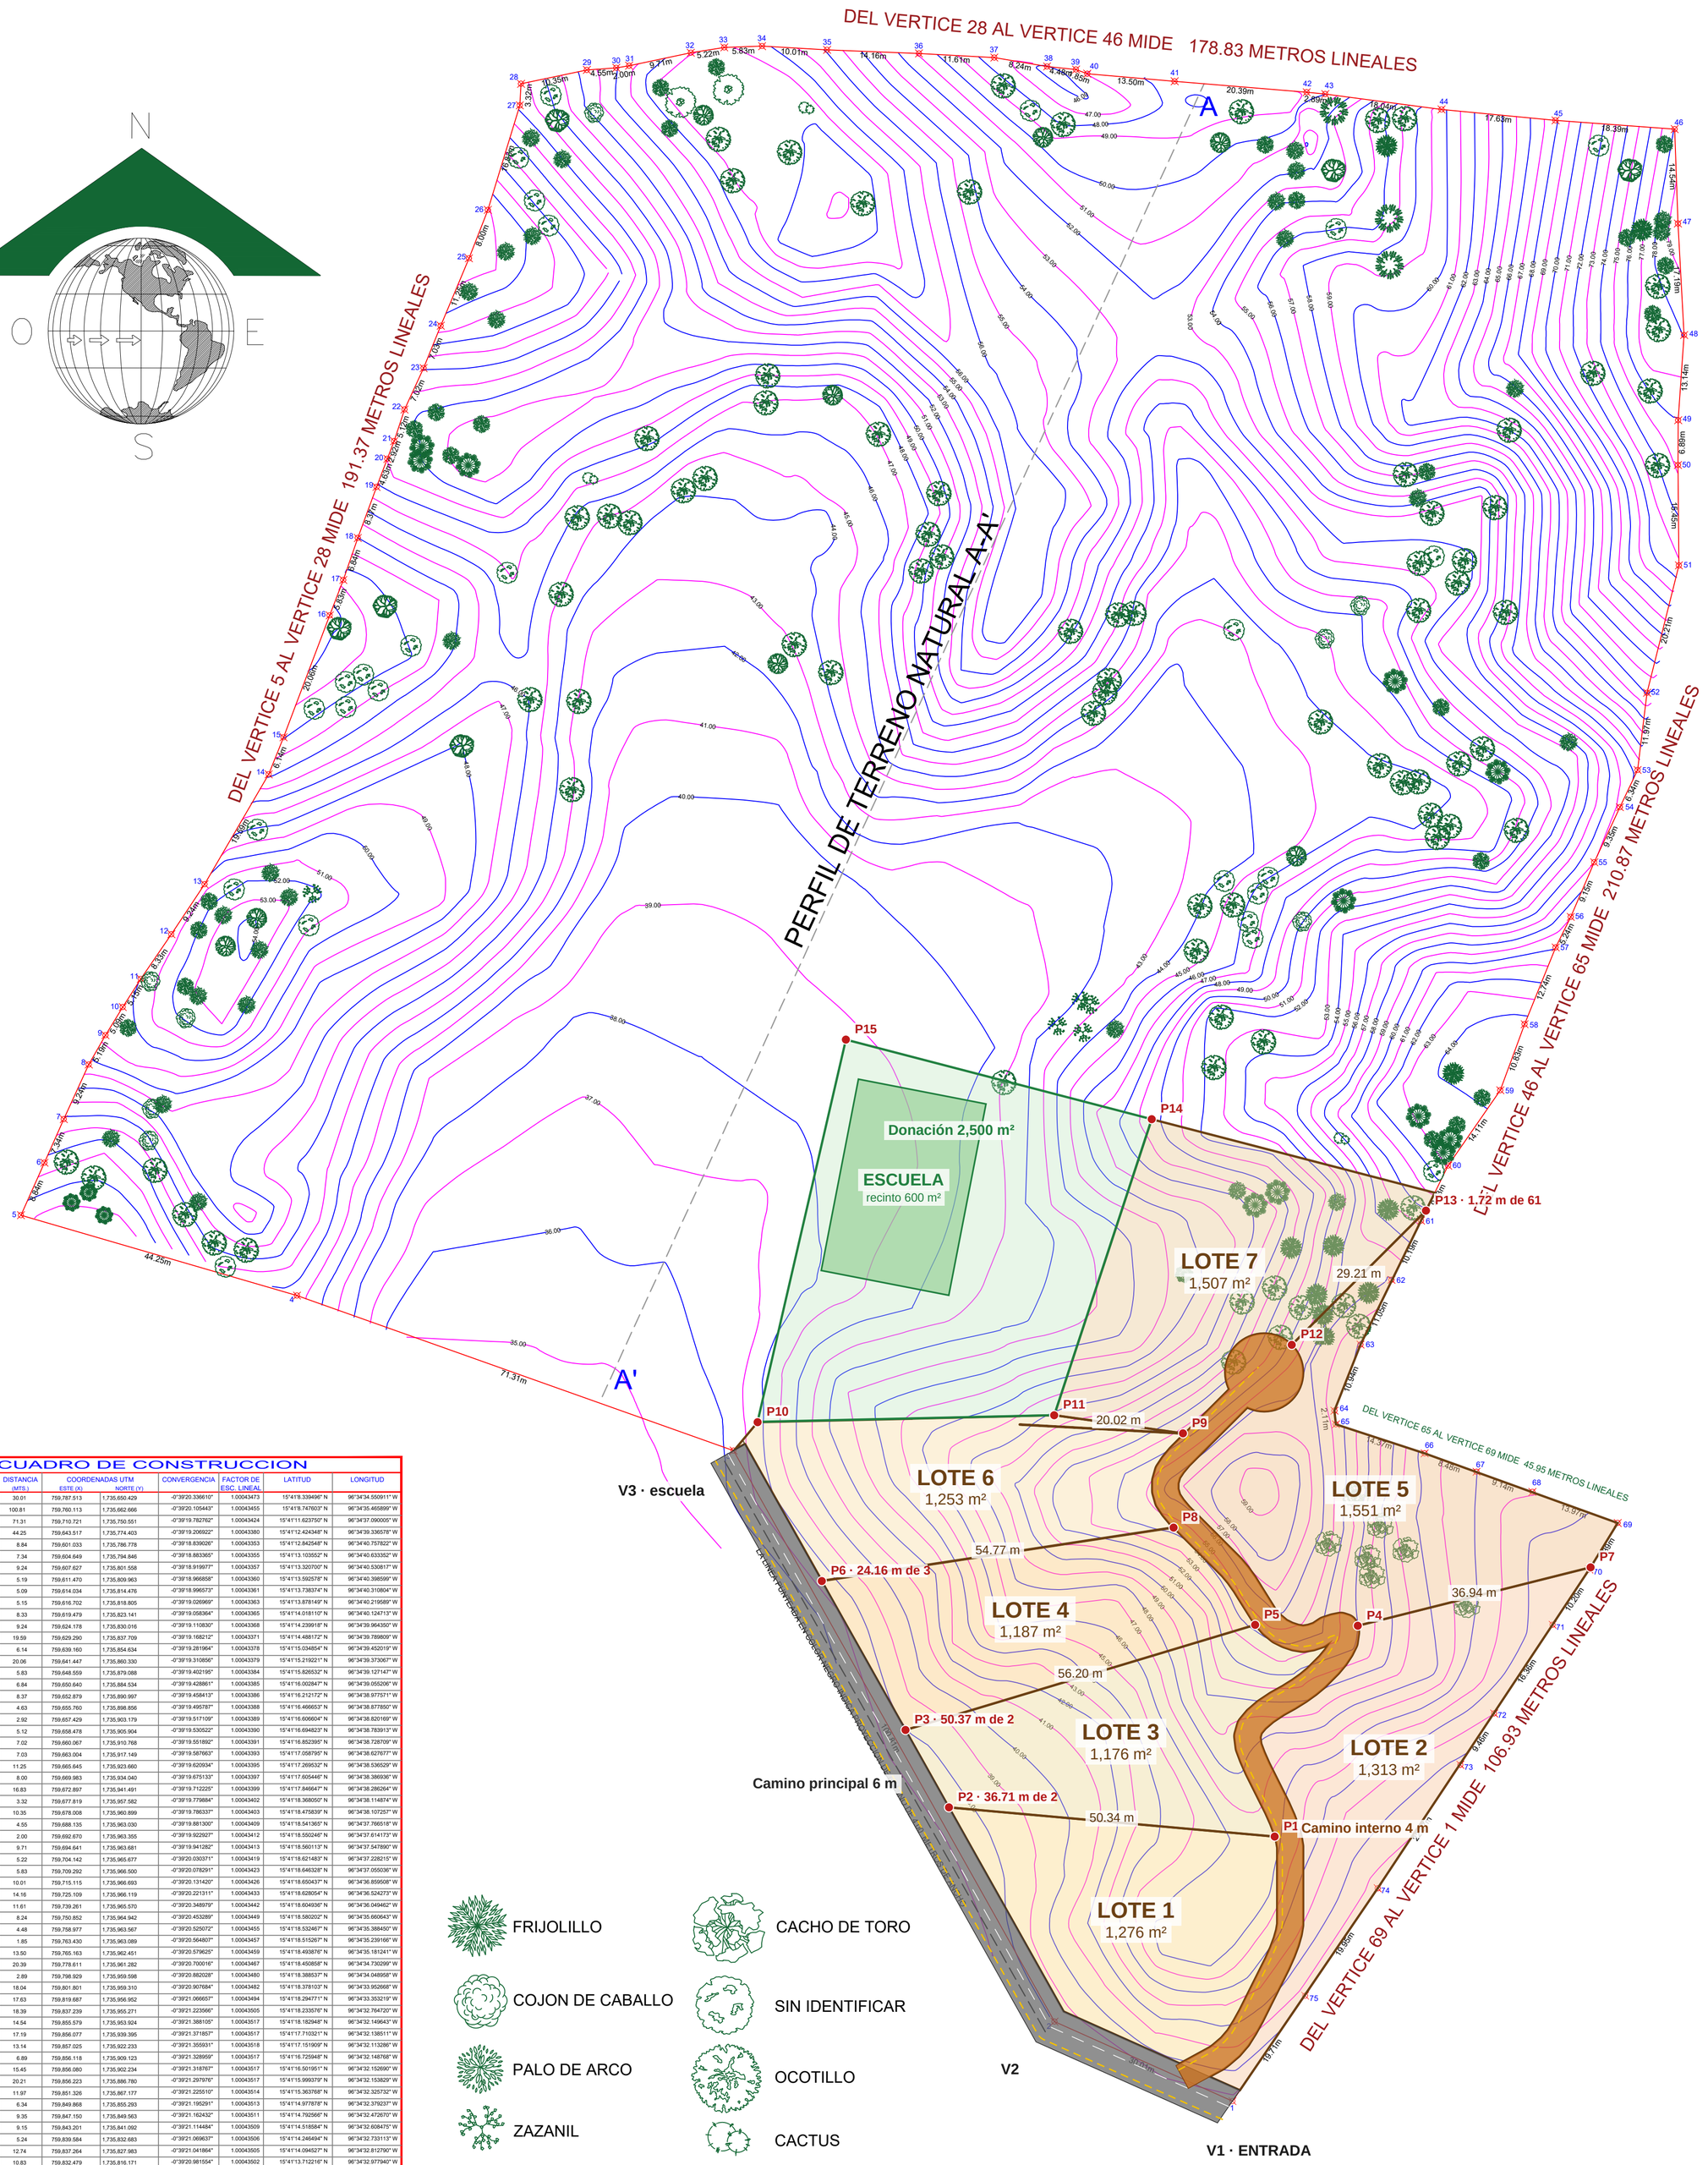



CUADRO DE CONSTRUCCION

LADO EST-PV	AZIMUT	DISTANCIA (MTS.)	COORDENADAS UTM ESTE (X)	NORTE (Y)	CONVERGENCIA	FACTOR DE ESC. LINEAL	LATITUD	LONGITUD
1-2	294°356.94"	30.01	759,787.513	1,735,650.429	-0°39'20.336610"	1.00043473	15°41'8.339496" N	96°34'34.550911" W
2-3	330°3949.32"	100.81	759,760.113	1,735,662.666	-0°39'20.105443"	1.00043455	15°41'8.747603" N	96°34'35.465899" W
3-4	289°3226.73"	71.31	759,710.721	1,735,750.551	-0°39'19.782762"	1.00043424	15°41'11.623750" N	96°34'37.090005" W
4-5	286°1424.39"	44.25	759,643.517	1,735,774.403	-0°39'19.206922"	1.00043380	15°41'12.424348" N	96°34'39.336578" W
5-6	24°829.27"	8.84	759,601.033	1,735,786.778	-0°39'18.839026"	1.00043353	15°41'12.842548" N	96°34'40.757822" W
6-7	23°5553.76"	7.34	759,604.649	1,735,794.846	-0°39'18.883365"	1.00043355	15°41'13.103552" N	96°34'40.633352" W
7-8	24°3416.32"	9.24	759,607.627	1,735,801.558	-0°39'18.919977"	1.00043357	15°41'13.320700" N	96°34'40.530817" W
8-9	29°368.96"	5.19	759,611.470	1,735,809.963	-0°39'18.966858"	1.00043360	15°41'13.592578" N	96°34'40.398599" W
9-10	31°3845.19"	5.09	759,614.034	1,735,814.476	-0°39'18.996573"	1.00043361	15°41'13.736374" N	96°34'40.318804" W
10-11	32°3815.41"	5.15	759,616.702	1,735,818.805	-0°39'19.026969"	1.00043363	15°41'13.878149" N	96°34'40.219589" W
11-12	34°218.11"	8.33	759,619.479	1,735,823.141	-0°39'19.058364"	1.00043365	15°41'14.018110" N	96°34'40.124713" W
12-13	33°3614.56"	9.24	759,624.178	1,735,830.016	-0°39'19.110830"	1.00043368	15°41'14.239918" N	96°34'39.964350" W
13-14	30°1456.65"	19.59	759,629.290	1,735,837.709	-0°39'19.168212"	1.00043371	15°41'14.488172" N	96°34'39.789809" W
14-15	21°5233.40"	6.14	759,639.160	1,735,854.634	-0°39'19.281964"	1.00043378	15°41'15.034854" N	96°34'39.452019" W
15-16	20°4550.28"	20.06	759,641.447	1,735,860.330	-0°39'19.310856"	1.00043379	15°41'15.219221" N	96°34'39.373067" W
16-17	20°5445.44"	5.83	759,648.559	1,735,879.088	-0°39'19.402195"	1.00043384	15°41'15.826532" N	96°34'39.127147" W
17-18	19°6'28.09"	6.84	759,650.640	1,735,884.534	-0°39'19.428861"	1.00043385	15°41'16.002847" N	96°34'39.055206" W
18-19	20°756.04"	8.37	759,652.879	1,735,890.997	-0°39'19.458413"	1.00043386	15°41'16.212172" N	96°34'38.975711" W
19-20	21°637.09"	4.63	759,655.760	1,735,898.856	-0°39'19.495787"	1.00043388	15°41'16.466653" N	96°34'38.877850" W
20-21	21°315.90"	2.92	759,657.429	1,735,903.179	-0°39'19.517109"	1.00043389	15°41'16.606604" N	96°34'38.820169" W
21-22	18°529.34"	5.12	759,658.478	1,735,905.904	-0°39'19.530522"	1.00043390	15°41'16.694823" N	96°34'38.783913" W
22-23	24°4255.17"	7.02	759,660.067	1,735,910.768	-0°39'19.551892"	1.00043391	15°41'16.852395" N	96°34'38.728709" W
23-24	22°442.67"	7.03	759,663.004	1,735,917.149	-0°39'19.587663"	1.00043393	15°41'17.058795" N	96°34'38.627677" W
24-25	22°4051.53"	11.25	759,665.645	1,735,923.660	-0°39'19.620934"	1.00043395	15°41'17.269532" N	96°34'38.536529" W
25-26	21°2135.62"	8.00	759,669.983	1,735,934.040	-0°39'19.675133"	1.00043397	15°41'17.605446" N	96°34'38.386936" W
26-27	17°029.16"	16.83	759,672.897	1,735,941.491	-0°39'19.712225"	1.00043399	15°41'17.846647" N	96°34'38.286264" W
27-28	03°1540.11"	3.32	759,677.819	1,735,957.582	-0°39'19.779884"	1.00043402	15°41'18.368050" N	96°34'38.114874" W
28-29	78°70.33"	10.35	759,678.008	1,735,960.899	-0°39'19.786337"	1.00043403	15°41'18.475839" N	96°34'38.107257" W
29-30	85°54'3.30"	4.55	759,688.135	1,735,963.030	-0°39'19.881300"	1.00043409	15°41'18.541365" N	96°34'37.766518" W
30-31	80°3630.25"	2.00	759,692.670	1,735,963.355	-0°39'19.922927"	1.00043412	15°41'18.550246" N	96°34'37.614173" W
31-32	78°8'8.37"	9.71	759,694.641	1,735,963.681	-0°39'19.941282"	1.00043413	15°41'18.560113" N	96°34'37.547890" W
32-33	80°55'14.06"	5.22	759,704.142	1,735,965.677	-0°39'20.030371"	1.00043419	15°41'18.621483" N	96°34'37.228215" W
33-34	88°65.97"	5.83	759,709.292	1,735,966.500	-0°39'20.078291"	1.00043423	15°41'18.646328" N	96°34'37.055036" W
34-35	93°1713.71"	10.01	759,715.115	1,735,966.693	-0°39'20.131420"	1.00043426	15°41'18.650437" N	96°34'36.859508" W
35-36	92°1317.64"	14.16	759,725.109	1,735,966.119	-0°39'20.221311"	1.00043433	15°41'18.628054" N	96°34'36.524273" W
36-37	93°64.50"	11.61	759,739.261	1,735,965.570	-0°39'20.348979"	1.00043442	15°41'18.604936" N	96°34'36.049462" W
37-38	99°3618.73"	8.24	759,750.852	1,735,964.942	-0°39'20.453289"	1.00043449	15°41'18.580202" N	96°34'35.660643" W
38-39	96°736.70"	4.48	759,758.977	1,735,963.567	-0°39'20.525072"	1.00043455	15°41'18.532467" N	96°34'35.388450" W
39-40	110°1239.85"	1.85	759,763.430	1,735,963.089	-0°39'20.564807"	1.00043457	15°41'18.515267" N	96°34'35.239166" W
40-41	94°585.11"	13.50	759,765.163	1,735,962.451	-0°39'20.579625"	1.00043459	15°41'18.493876" N	96°34'35.181241" W
41-42	94°44'16.69"	20.39	759,778.611	1,735,961.282	-0°39'20.700016"	1.00043467	15°41'18.450858" N	96°34'34.730299" W
42-43	95°43'35.02"	2.89	759,798.929	1,735,959.598	-0°39'20.882028"	1.00043480	15°41'18.388537" N	96°34'34.048958" W
43-44	97°3036.99"	18.04	759,801.801	1,735,959.310	-0°39'20.907684"	1.00043482	15°41'18.378103" N	96°34'33.952668" W
44-45	95°2814.44"	17.63	759,819.687	1,735,956.952	-0°39'21.066657"	1.00043494	15°41'18.294771" N	96°34'33.353219" W
45-46	94°122.18"	18.39	759,837.239	1,735,955.271	-0°39'21.223566"	1.00043505	15°41'18.233576" N	96°34'32.764720" W
46-47	178°212.78"	14.54	759,855.579	1,735,953.924	-0°39'21.388105"	1.00043517	15°41'18.182948" N	96°34'32.149643" W
47-48	176°5017.85"	17.19	759,856.077	1,735,939.395	-0°39'21.371857"	1.00043517	15°41'17.710321" N	96°34'32.138511" W
48-49	183°5727.49"	13.14	759,857.025	1,735,922.233	-0°39'21.355931"	1.00043518	15°41'17.151909" N	96°34'32.113286" W
49-50	180°1857.75"	6.89	759,856.118	1,735,909.123	-0°39'21.328959"	1.00043517	15°41'16.725948" N	96°34'32.148768" W
50-51	179°2811.43"	15.45	759,856.080	1,735,902.234	-0°39'21.318767"	1.00043517	15°41'16.501951" N	96°34'32.152690" W
51-52	194°133.34"	20.21	759,856.223	1,735,886.780	-0°39'21.297976"	1.00043517	15°41'15.999379" N	96°34'32.153829" W
52-53	186°5939.96"	11.97	759,851.326	1,735,867.177	-0°39'21.225510"	1.00043514	15°41'15.363768" N	96°34'32.325732" W
53-54	205°2237.62"	6.34	759,849.868	1,735,855.293	-0°39'21.195291"	1.00043513	15°41'14.977878" N	96°34'32.379237" W
54-55	204°5938.15"	9.35	759,847.150	1,735,849.563	-0°39'21.162432"	1.00043511	15°41'14.792566" N	96°34'32.472670" W
55-56	203°1627.13"	9.15	759,843.201	1,735,841.092	-0°39'21.114484"	1.00043509	15°41'14.518584" N	96°34'32.608475" W
56-57	206°1618.23"	5.24	759,839.584	1,735,832.683	-0°39'21.069637"	1.00043506	15°41'14.246494" N	96°34'32.733113" W
57-58	202°39.71"	12.74	759,837.264	1,735,827.983	-0°39'21.041864"	1.00043505	15°41'14.094527" N	96°34'32.812790" W
58-59	200°1124.40"	10.83	759,832.479	1,735,816.171	-0°39'20.981554"	1.00043502	15°41'13.712216" N	96°34'32.977940" W
59-60	214°4047.10"	14.11	759,828.741	1,735,806.006	-0°39'20.933101"	1.00043499	15°41'13.383070" N	96°34'33.107313" W
60-61	206°1726.48"	9.43	759,820.710	1,735,794.399	-0°39'20.843625"	1.00043494	15°41'13.008633" N	96°34'33.381336" W
61-62	206°3156.45"	10.19	759,816.532	1,735,785.942	-0°39'20.793621"	1.00043492	15°41'12.735191" N	96°34'33.524822" W
62-63	205°3313.91"	11.05	759,811.982	1,735,776.829	-0°39'20.739303"	1.00043489	15°41'12.440556" N	96°34'33.681046" W
63-64	201°3158.43"	10.94	759,807.216	1,735,766.861	-0°39'20.681804"	1.00043486	15°41'12.118199" N	96°34'33.844848" W
64-65	173°4553.42"	2.11	759,803.202	1,735,756.688	-0°39'20.630837"	1.00043483	15°41'11.788896" N	96°34'33.983487" W
65-66	108°536.04"	14.37	759,803.431	1,735,754.592	-0°39'20.629920"	1.00043483	15°41'11.720655" N	96°34'33.976606" W
66-67	109°3552.42"	8.48	759,817.094	1,735,750.128	-0°39'20.747538"	1.00043492	15°41'11.570413" N	96°34'33.519717" W
67-68	109°4733.03"	9.14	759,825.079	1,735,747.285	-0°39'20.815942"	1.00043497	15°41'11.474995" N	96°34'33.252790" W
68-69	110°150.78"	13.97	759,833.682	1,735,744.189	-0°39'20.889592"	1.00043503	15°41'11.371120" N	96°34'32.965217" W
69-70	211°2712.72"	8.39	759,846.804	1,735,739.405	-0°39'21.001842"	1.00043511	15°41'11.210674" N	96°34'32.526610" W
70-71	213°335.22"	10.20	759,842.428	1,735,732.251	-0°39'20.951903"	1.00043508	15°41'10.979675" N	96°34'32.676241" W
71-72	213°2337.55"	16.36	759,836.789	1,735,723.748	-0°39'20.888574"	1.00043505	15°41'10.705281" N	96°34'32.868783" W
72-73	213°2333.55"	9.46	759,827.786	1,735,710.091	-0°39'20.787351"	1.00043499	15°41'10.264545" N	96°34'33.176218" W
73-74	213°4744.49"	22.87	759,822.581	1,735,702.195	-0°39'20.728830"	1.00043495	15°41'10.009727" N	96°34'33.353959" W
74-75	214°3717.56"	19.95	759,809.861	1,735,683.191	-0°39'20.586235"	1.00043487	15°41'9.396506" N	96°34'33.788210" W
75-76	214°3747.06"	19.71	759,798.689	1,735,666.662	-0°39'20.461229"	1.00043480	15°41'8.863187" N	96°34'34.169551" W
AREA = 48,858.49 m2			PERIMETRO = 980.34 m					

- FRIJOLILLO
- COJON DE CABALLO
- PALO DE ARCO
- ZAZANIL
- MULATO
- CIRUELO
- QUEBRACHO
- CACHO DE TORO
- SIN IDENTIFICAR
- OCOTILLO
- CACTUS
- GUAYACAN
- CAMARON

AREA = 48,858.49 m2

PERIMETRO = 980.34 m

PROYECTO TOPOGRÁFICO PLANIMETRIA

ESCALA: LA INDICADA
ACOTACIONES: EN M.
FECHA: MAYO 2022
PROPIETARIO: SR. CARLOS

LEVANTÓ Y PROYECTÓ: ING. JESUS MENDEZ SALINAS.
CED. PROF: 3141693
PLANO: 1 DE 3

SIMBOLOGÍA

- PERFIL A-A' DE TERRENO NATURAL
- CURVAS GRUESAS A CADA 2.00m
- CURVAS DELGADAS A CADA 1.00m
- 1 — POLÍGONO GENERAL, NÚMERO DE LINDERO MEDIDO
- INDICA LINDERO MEDIDO
- 30.01m — NOMENCLATURA DE MEDIDAS DE LOS LADOS DEL POLIGONO
- 45.00 — NOMENCLATURA DE ELEVACION DE CURVA DE NIVEL SOBRE EL NIVEL DEL MAR
- PROYECCION DE CAMINO

DATOS DEL PROYECTO

TRABAJO REALIZADO CON EQUIPO TOPOGRAFICO HI-TARGET ZTS 320 R

DIRECCION: ZAPOTAL, TONAMECA, POCHUTLA, OAXACA, MEXICO

DISTRITO: 30 POCHUTLA

REGIÓN: COSTA

COORDENADAS: UTM
ZONA : HEMISFERIO NORTE 14
DATUM: WGS 84


MICROLOCALIZACIÓN

MACROLOCALIZACIÓN



ZAPOTAL · PROPUESTA DE LOTES Y CAMINOS (opción A)

Sobre la planta topográfica del Ing. Jesús Méndez Salinas (mayo 2022). Curvas a cada 1 m.

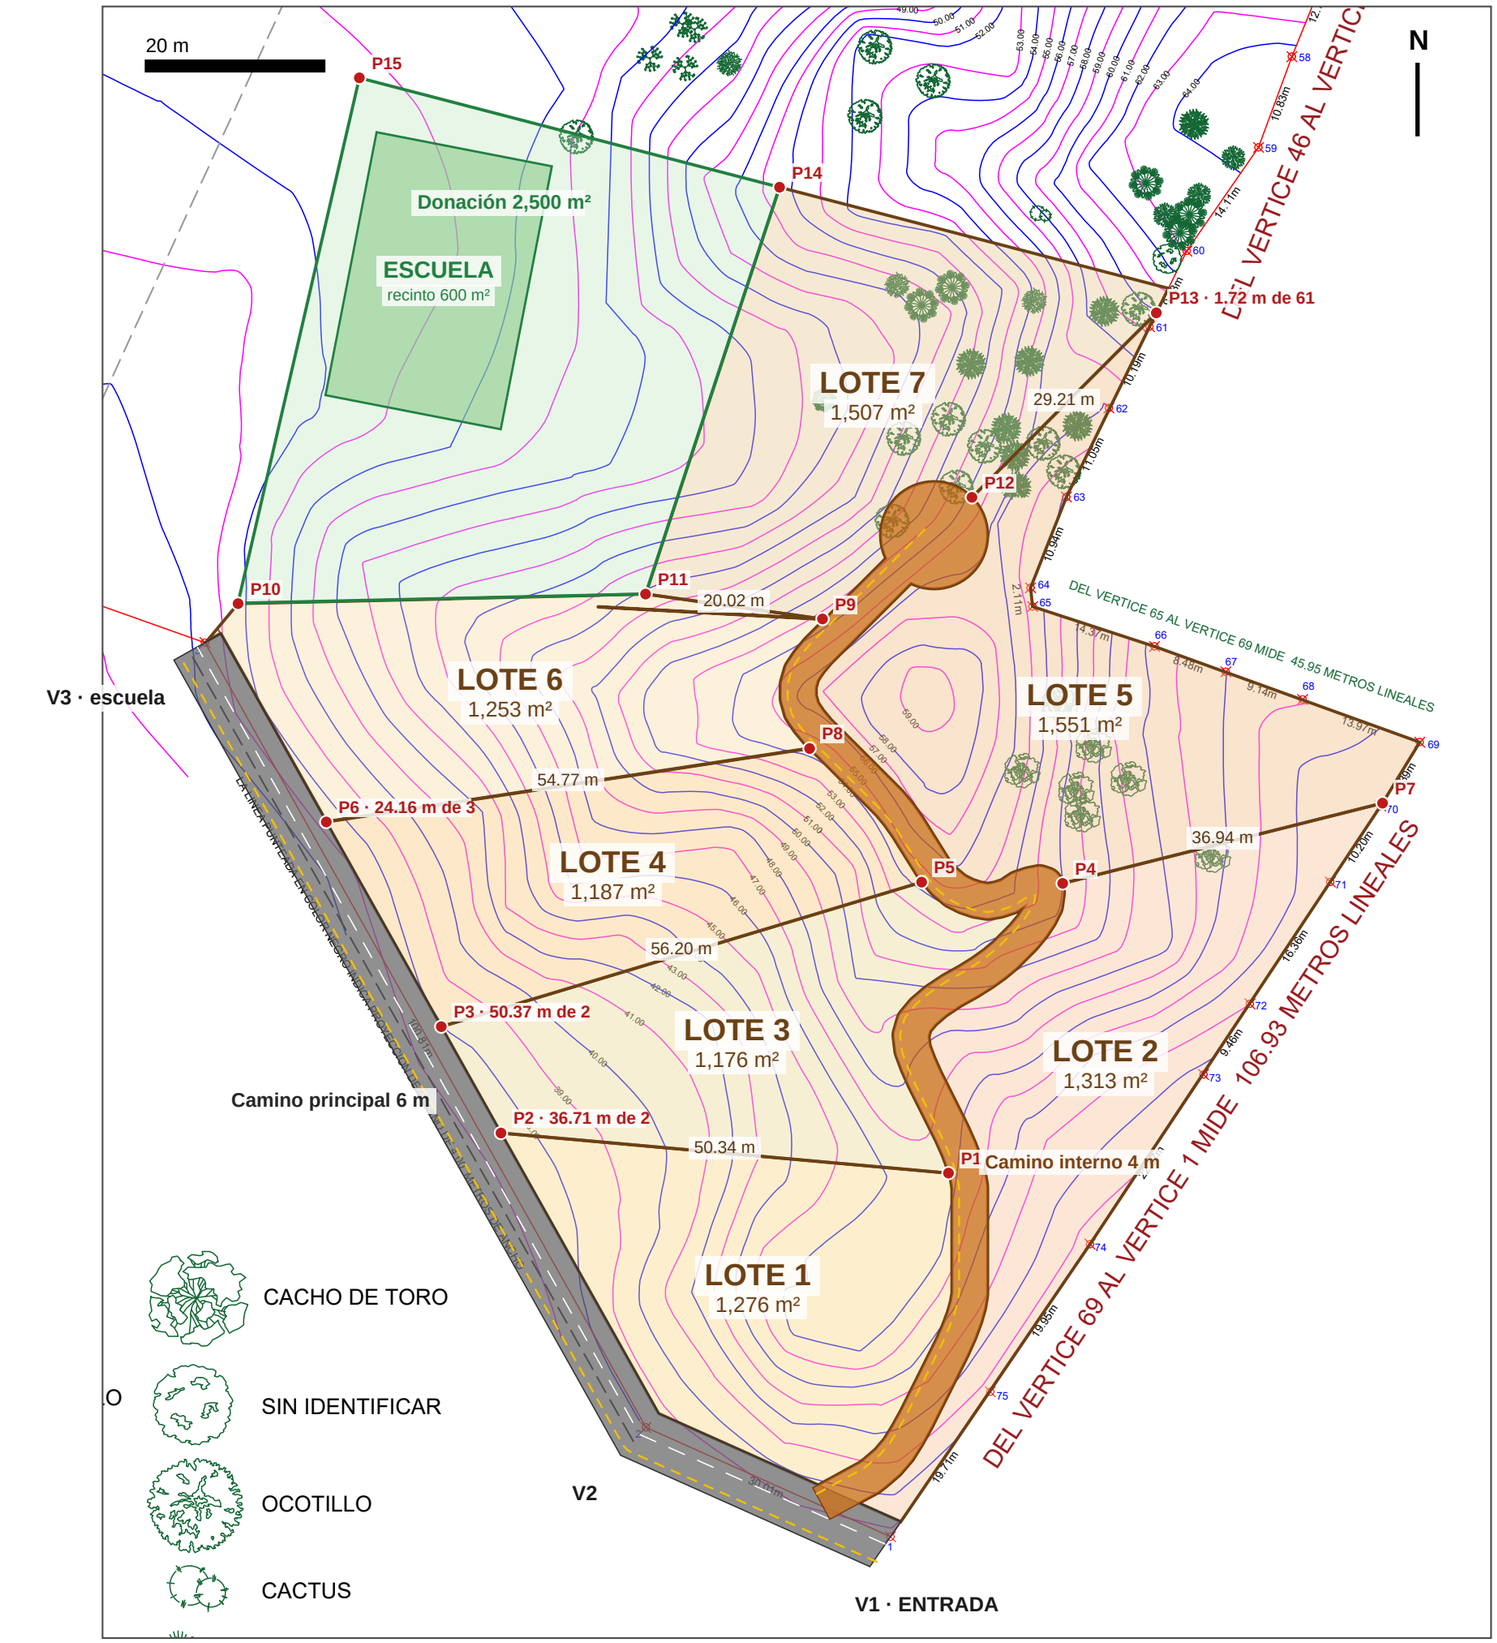

SIMBOLOGÍA · PROPUESTA DE LOTES Y CAMINOS

- Camino principal 6 m (V1·V2·V3): 2 m en el predio + 4 m del vecino
- Camino interno privado 4 m: 147 m, retorno de 12 m de diámetro
- Línea eléctrica propuesta
- Punto a marcar por el topógrafo (ver tabla)
- Lote (7 lotes)
- Escuela Tribu: recinto 600 m² en la donación de 2,500 m²

LOTES

Lote	Superficie	Vista al mar	Frente al camino
1	1,276 m²	sí	42 m
2	1,313 m²	sí	83 m
3	1,176 m²	sí	51 m
4	1,187 m²	sí	21 m
5	1,551 m²	amplia	73 m
6	1,253 m²	amplia	18 m
7	1,507 m²	no	28 m

Total en lotes	**9,263 m²**
Camino interno 4 m	**667 m²**
Camino principal 6 m (en el predio)	**261 m²**
Donación escuela	**2,500 m²**

Números rojos en el lindero (1, 74, 75·) = vértices medidos del levantamiento, no metros.
Cada línea entre lotes es recta, de un punto P al otro; su largo está escrito en la línea.
Camino interno: pendiente máxima ~22% en tramos cortos (promedio 13%).
Concreto hidráulico recomendado en los tramos de más de 15%.
Propuesta preliminar. Linderos, huellas y pendientes se confirman con topógrafo antes de vender o construir.

PUNTOS PARA EL TOPÓGRAFO (UTM 14N, WGS 84)

Punto	Este	Norte	Referencia
P1	759794.00	1735691.15	borde del camino interno 4 m
P2	759743.87	1735695.64	a 36.71 m del vért. 2 hacia el 3, 2.0 m adentro (borde camino 6 m)
P3	759737.18	1735707.55	a 50.37 m del vért. 2 hacia el 3, 2.0 m adentro (borde camino 6 m)
P4	759806.80	1735723.59	borde del camino interno 4 m
P5	759791.00	1735723.73	borde del camino interno 4 m
P6	759724.30	1735730.47	a 24.16 m del vért. 3 hacia el 2, 2.0 m adentro (borde camino 6 m)
P7	759842.63	1735732.58	coincide con el vértice 70 del levantamiento
P8	759778.44	1735738.70	borde del camino interno 4 m
P9	759779.89	1735753.20	borde del camino interno 4 m
P10	759714.42	1735754.92	esquina de la donación
P11	759760.07	1735755.99	esquina de la donación
P12	759796.63	1735766.82	borde del camino interno 4 m
P13	759817.29	1735787.48	sobre el lindero, a 1.72 m del vért. 61 hacia el 60
P14	759775.08	1735801.55	esquina de la donación
P15	759728.00	1735813.80	esquina de la donación